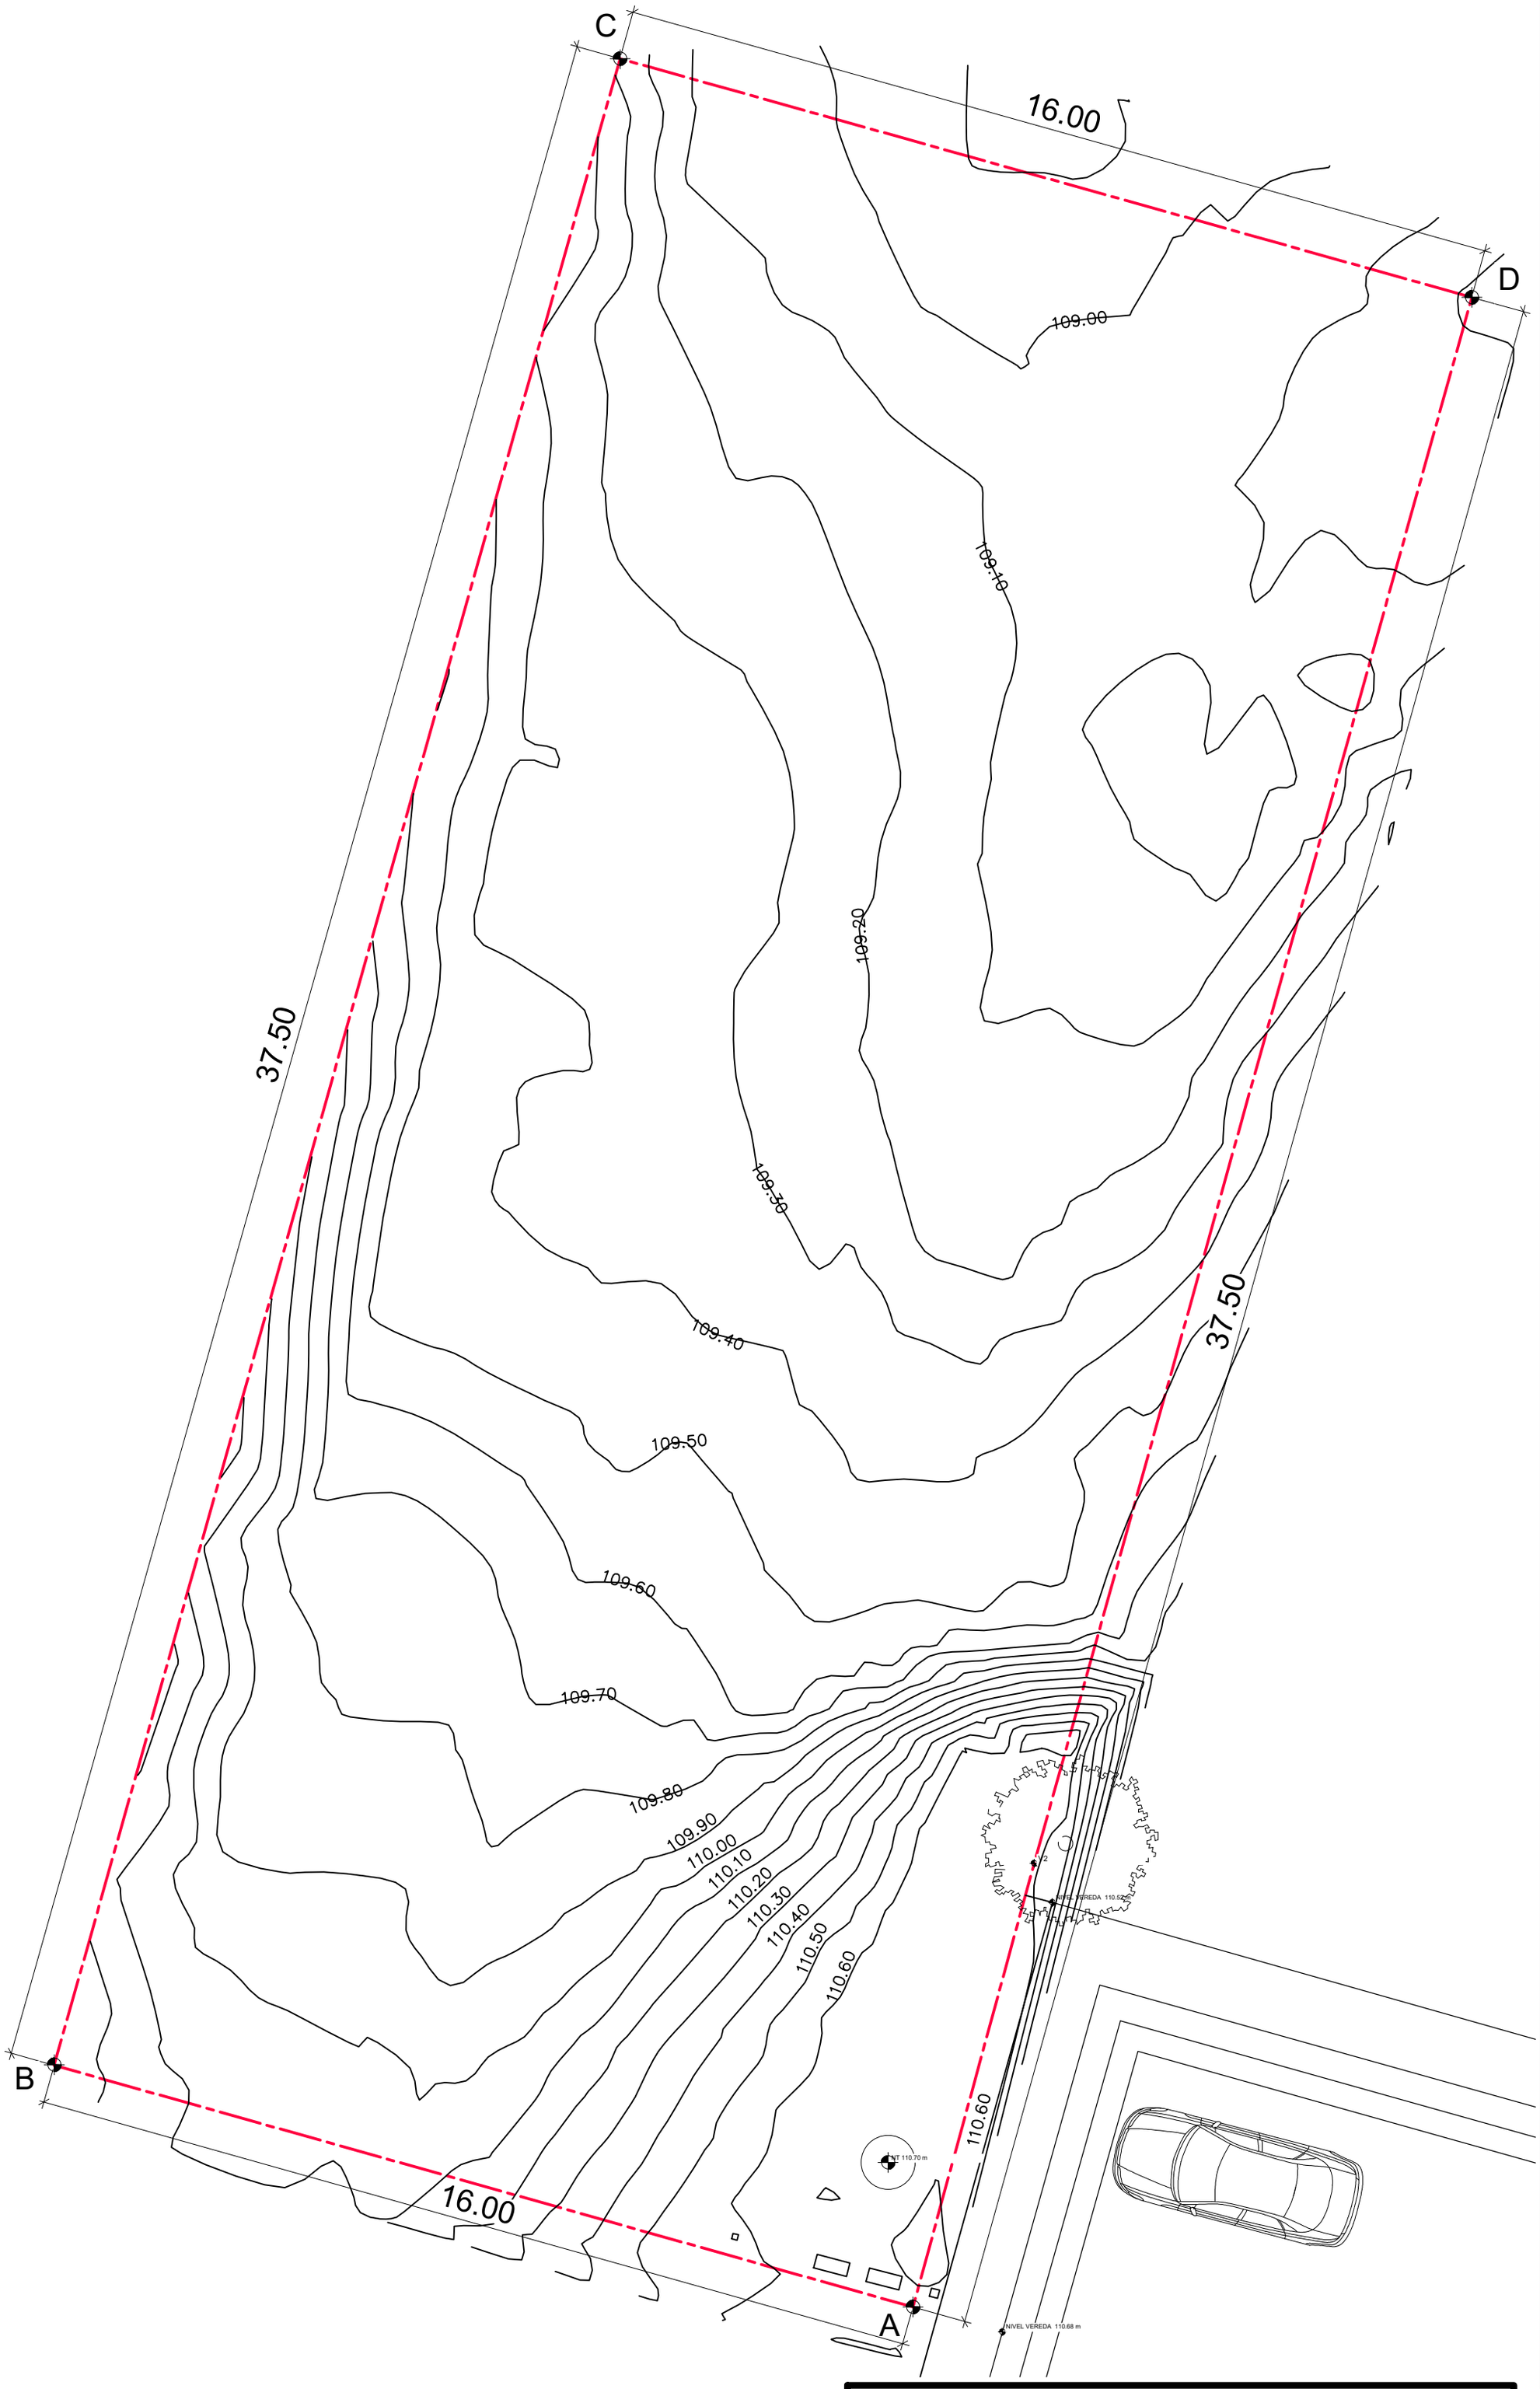

POLÍGONO LOTE 141 A-B-C-D-A = 600 m²			
TRAMO	A-B	=	16 Mts
TRAMO	B-C	=	37.5 Mts
TRAMO	C-D	=	16 Mts
TRAMO	D-A	=	37.5 Mts

E1/100

LEVANTAMIENTO TOPOGRÁFICO 09|2025

UBICACIÓN: AVENIDA CUATRO ESQUINAS 4500, CONDOMINIO UMBRALES

PROPIETARIOS:

ROLES DE LAS PROPIEDADES : LOTE 141

LAM. 1 | 1

ARQUITECTO | FÉLIX ALVAYAI ROJAS | FAALVAYAI@UC.CL